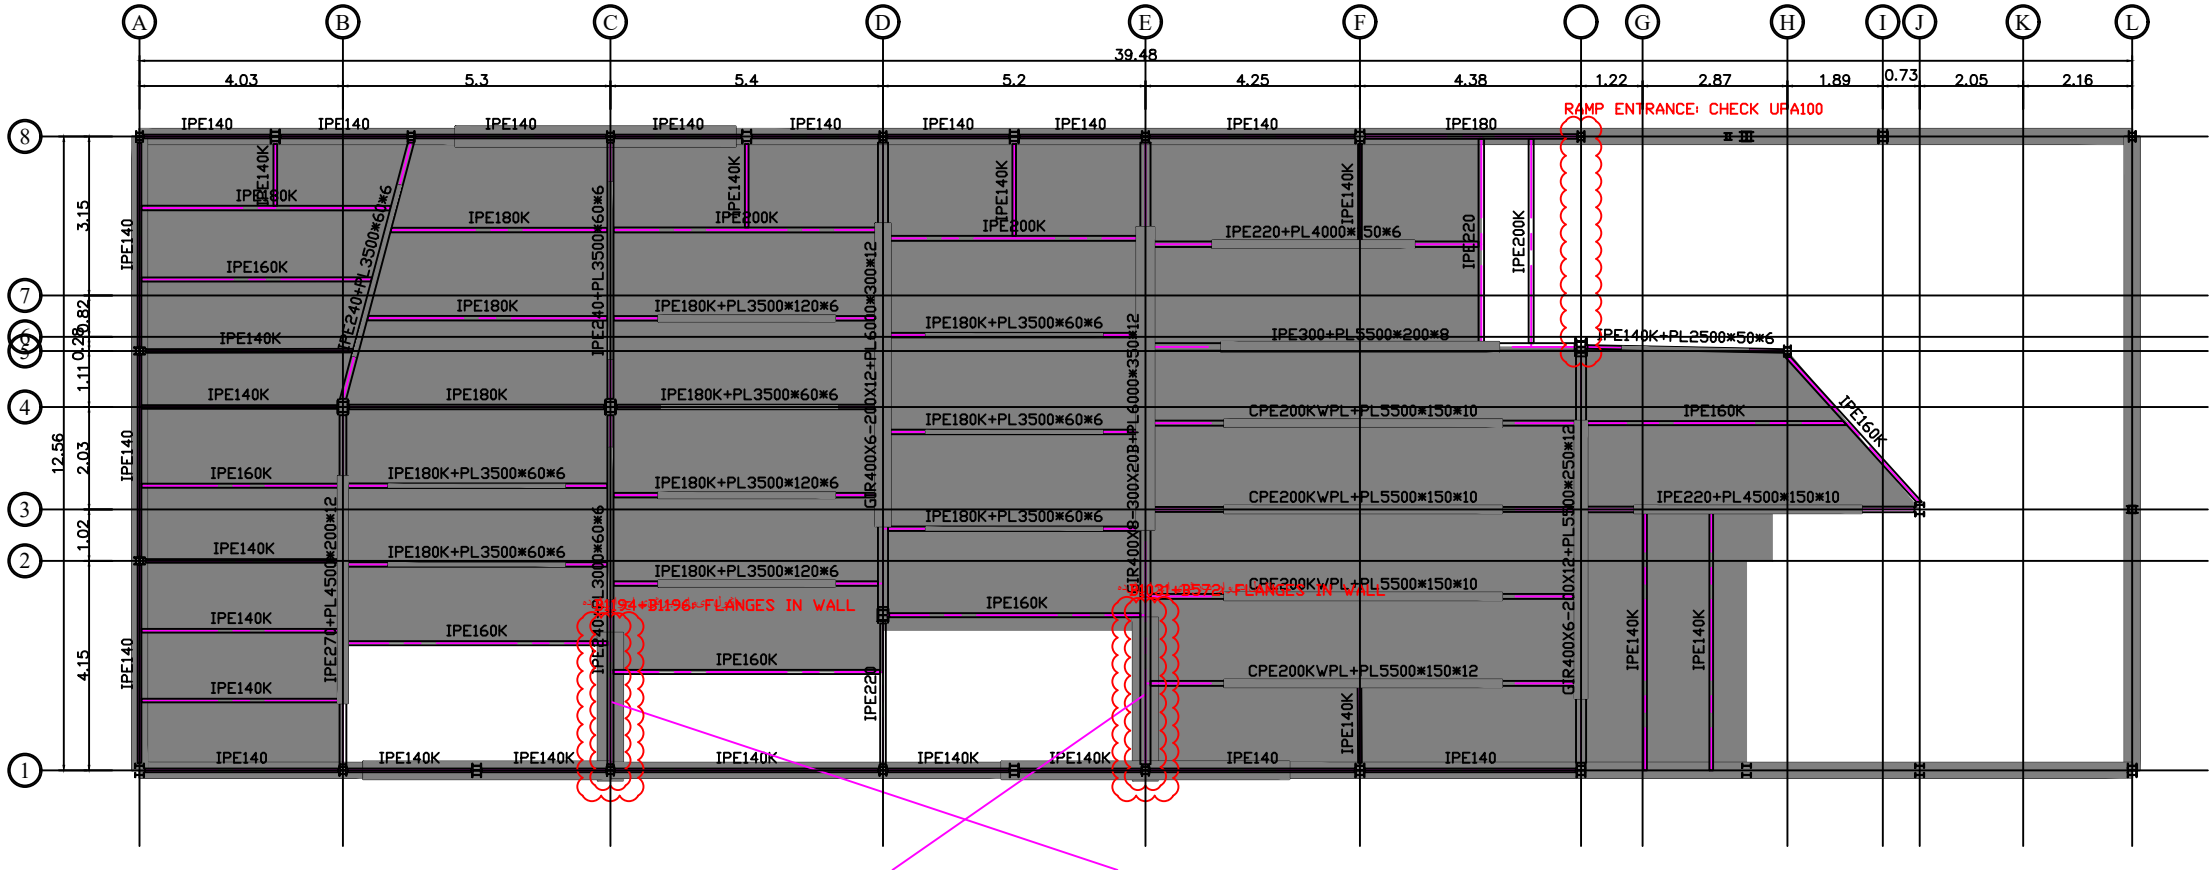

A
B
C
D
E
F
G
H
I
J
K
L
39.48
4.03
5.3
5.4
5.2
4.25
4.38
1.22
2.87
1.89
0.73
2.05
2.16
8
7
6
5
4
3
2
1
3.15
0.82
0.28
1.11
2.03
1.02
4.15
12.56
RAMP ENTRANCE: CHECK UPA100
IPE140
IPE180
IPE200
IPE220
IPE160
IPE140K
IPE160K
IPE180K
IPE200K
IPE220K
IPE240+PL3500*6
IPE270+PL4500*200*12
IPE240+PL3000*60*6
GIR400X6-200X12+PL6000*300*12
GIR400X8-300X20B+PL6000*350*12
GIR400X6-200X12+PL5500*250*12
IPE180K+PL3500*120*6
IPE180K+PL3500*60*6
IPE220+PL4000*150*6
IPE300+PL5500*200*8
IPE140K+PL2500*50*6
CPE200KWPL+PL5500*150*10
IPE220+PL4500*150*10
CPE200KWPL+PL5500*150*12
FLANGES IN WALL